


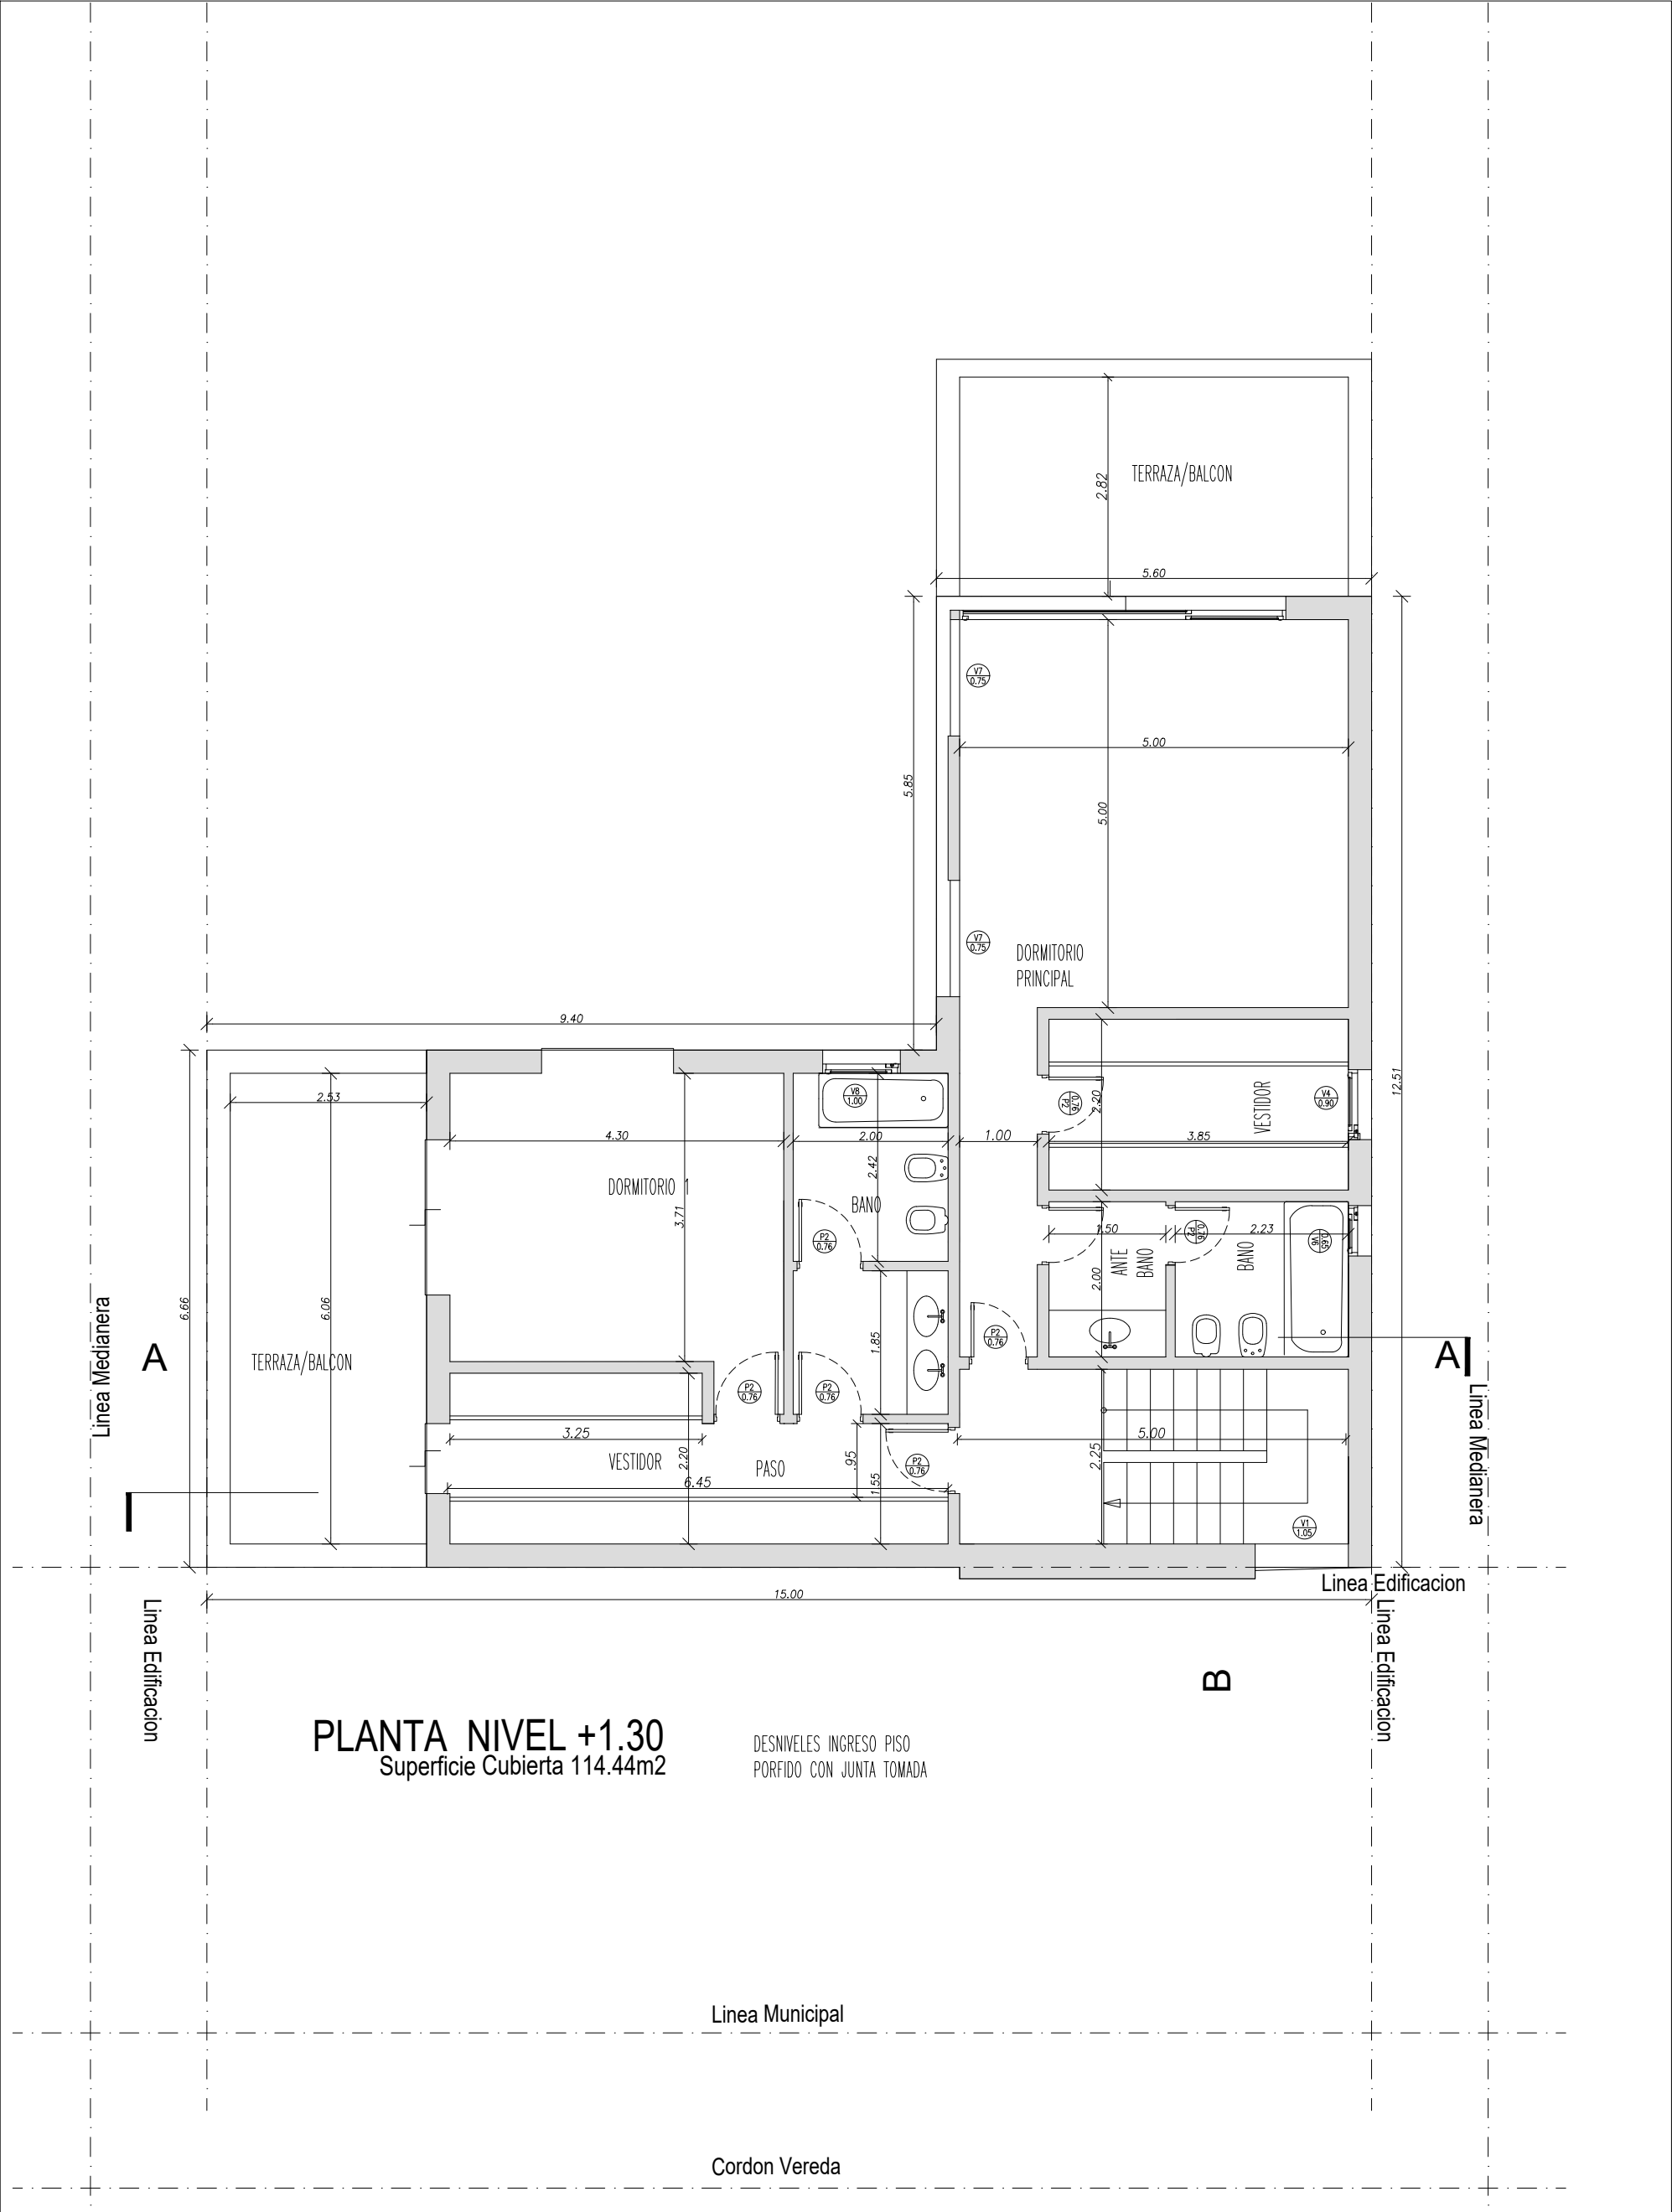

				Obra:	Plano/Especialidad	Desig. plano:
				VIVIENDA UNIFAMILIAR	ARQUITECTURA	
				Ubicación:	Contenidos:	A02
Fecha: 31-08-2010	Escala: 1:75	Desarrollo:	Observ.:	COSTA AZUL CORDOBA	PLANTA NIVEL-1.30	
						Version.: 11