


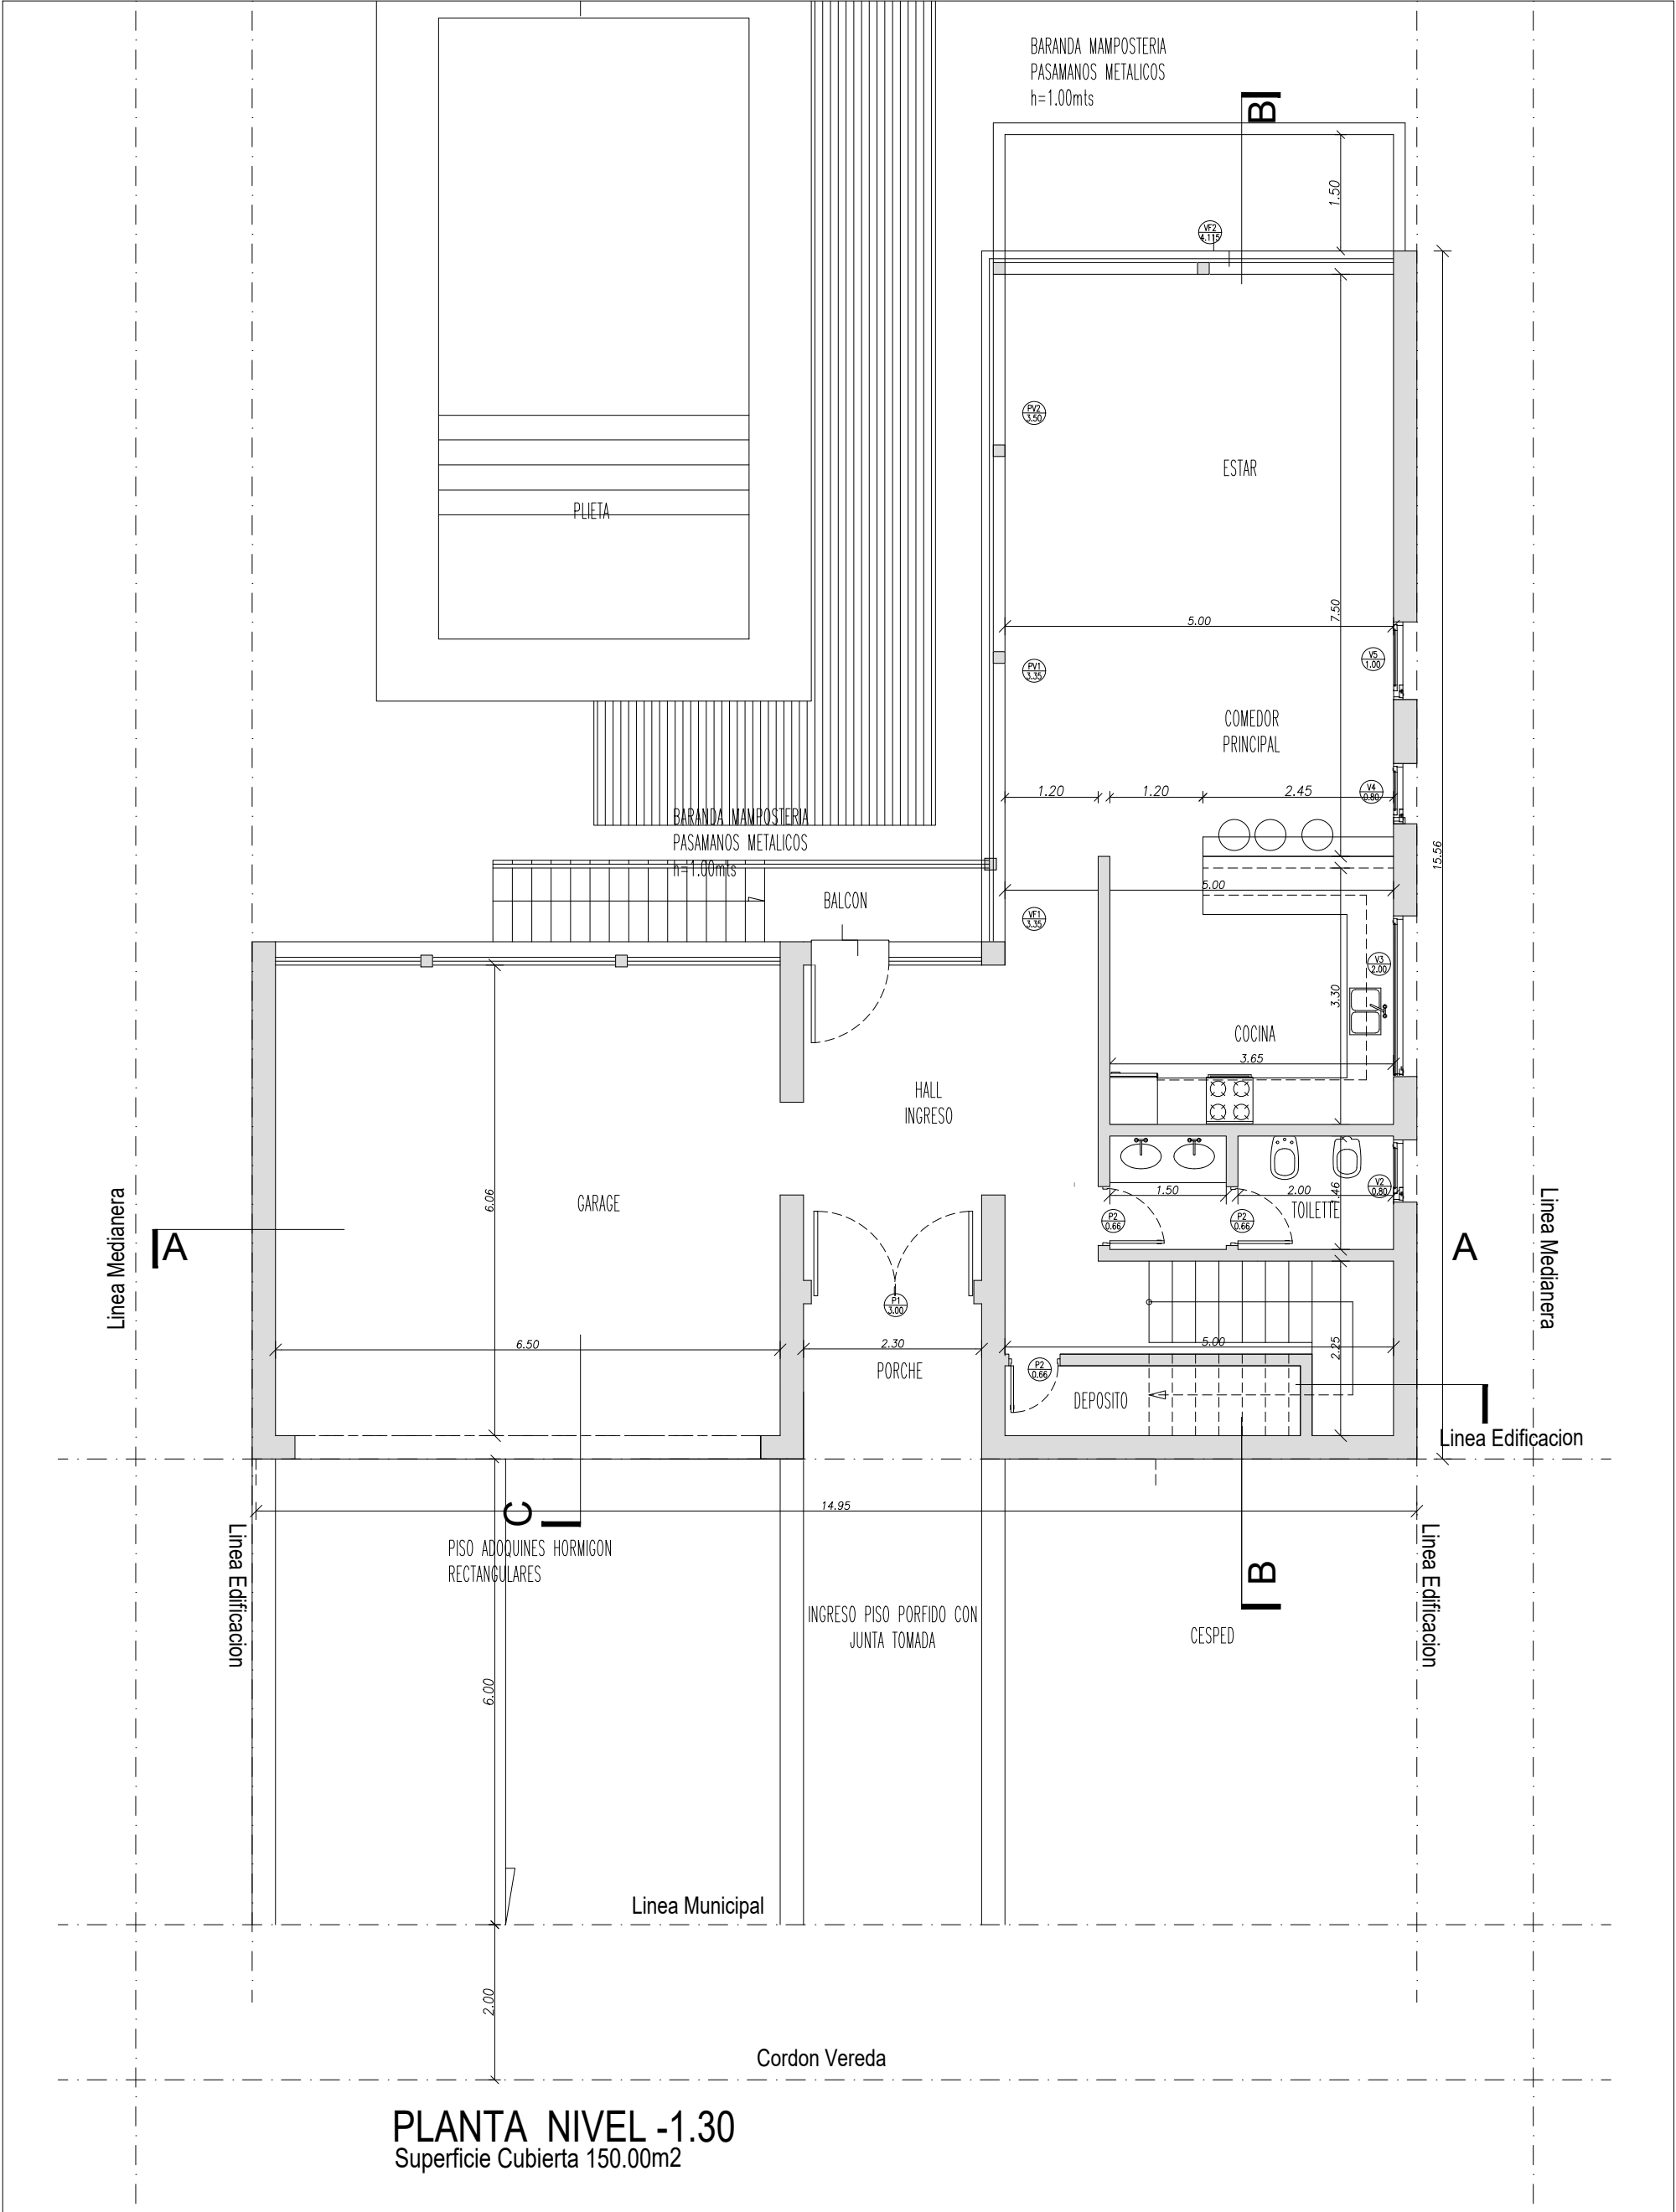

				Obra: VIVIENDA UNIFAMILIAR	Plano/Especialidad ARQUITECTURA	Desig. plano: A01
				Ubicación: COSTA AZUL CORDOBA	Contenidos: PLANTA NIVEL-4.80	
Fecha: 31-08-2010	Escala: 1:75	Desarrollo:	Observ.:	Version.: 11		