


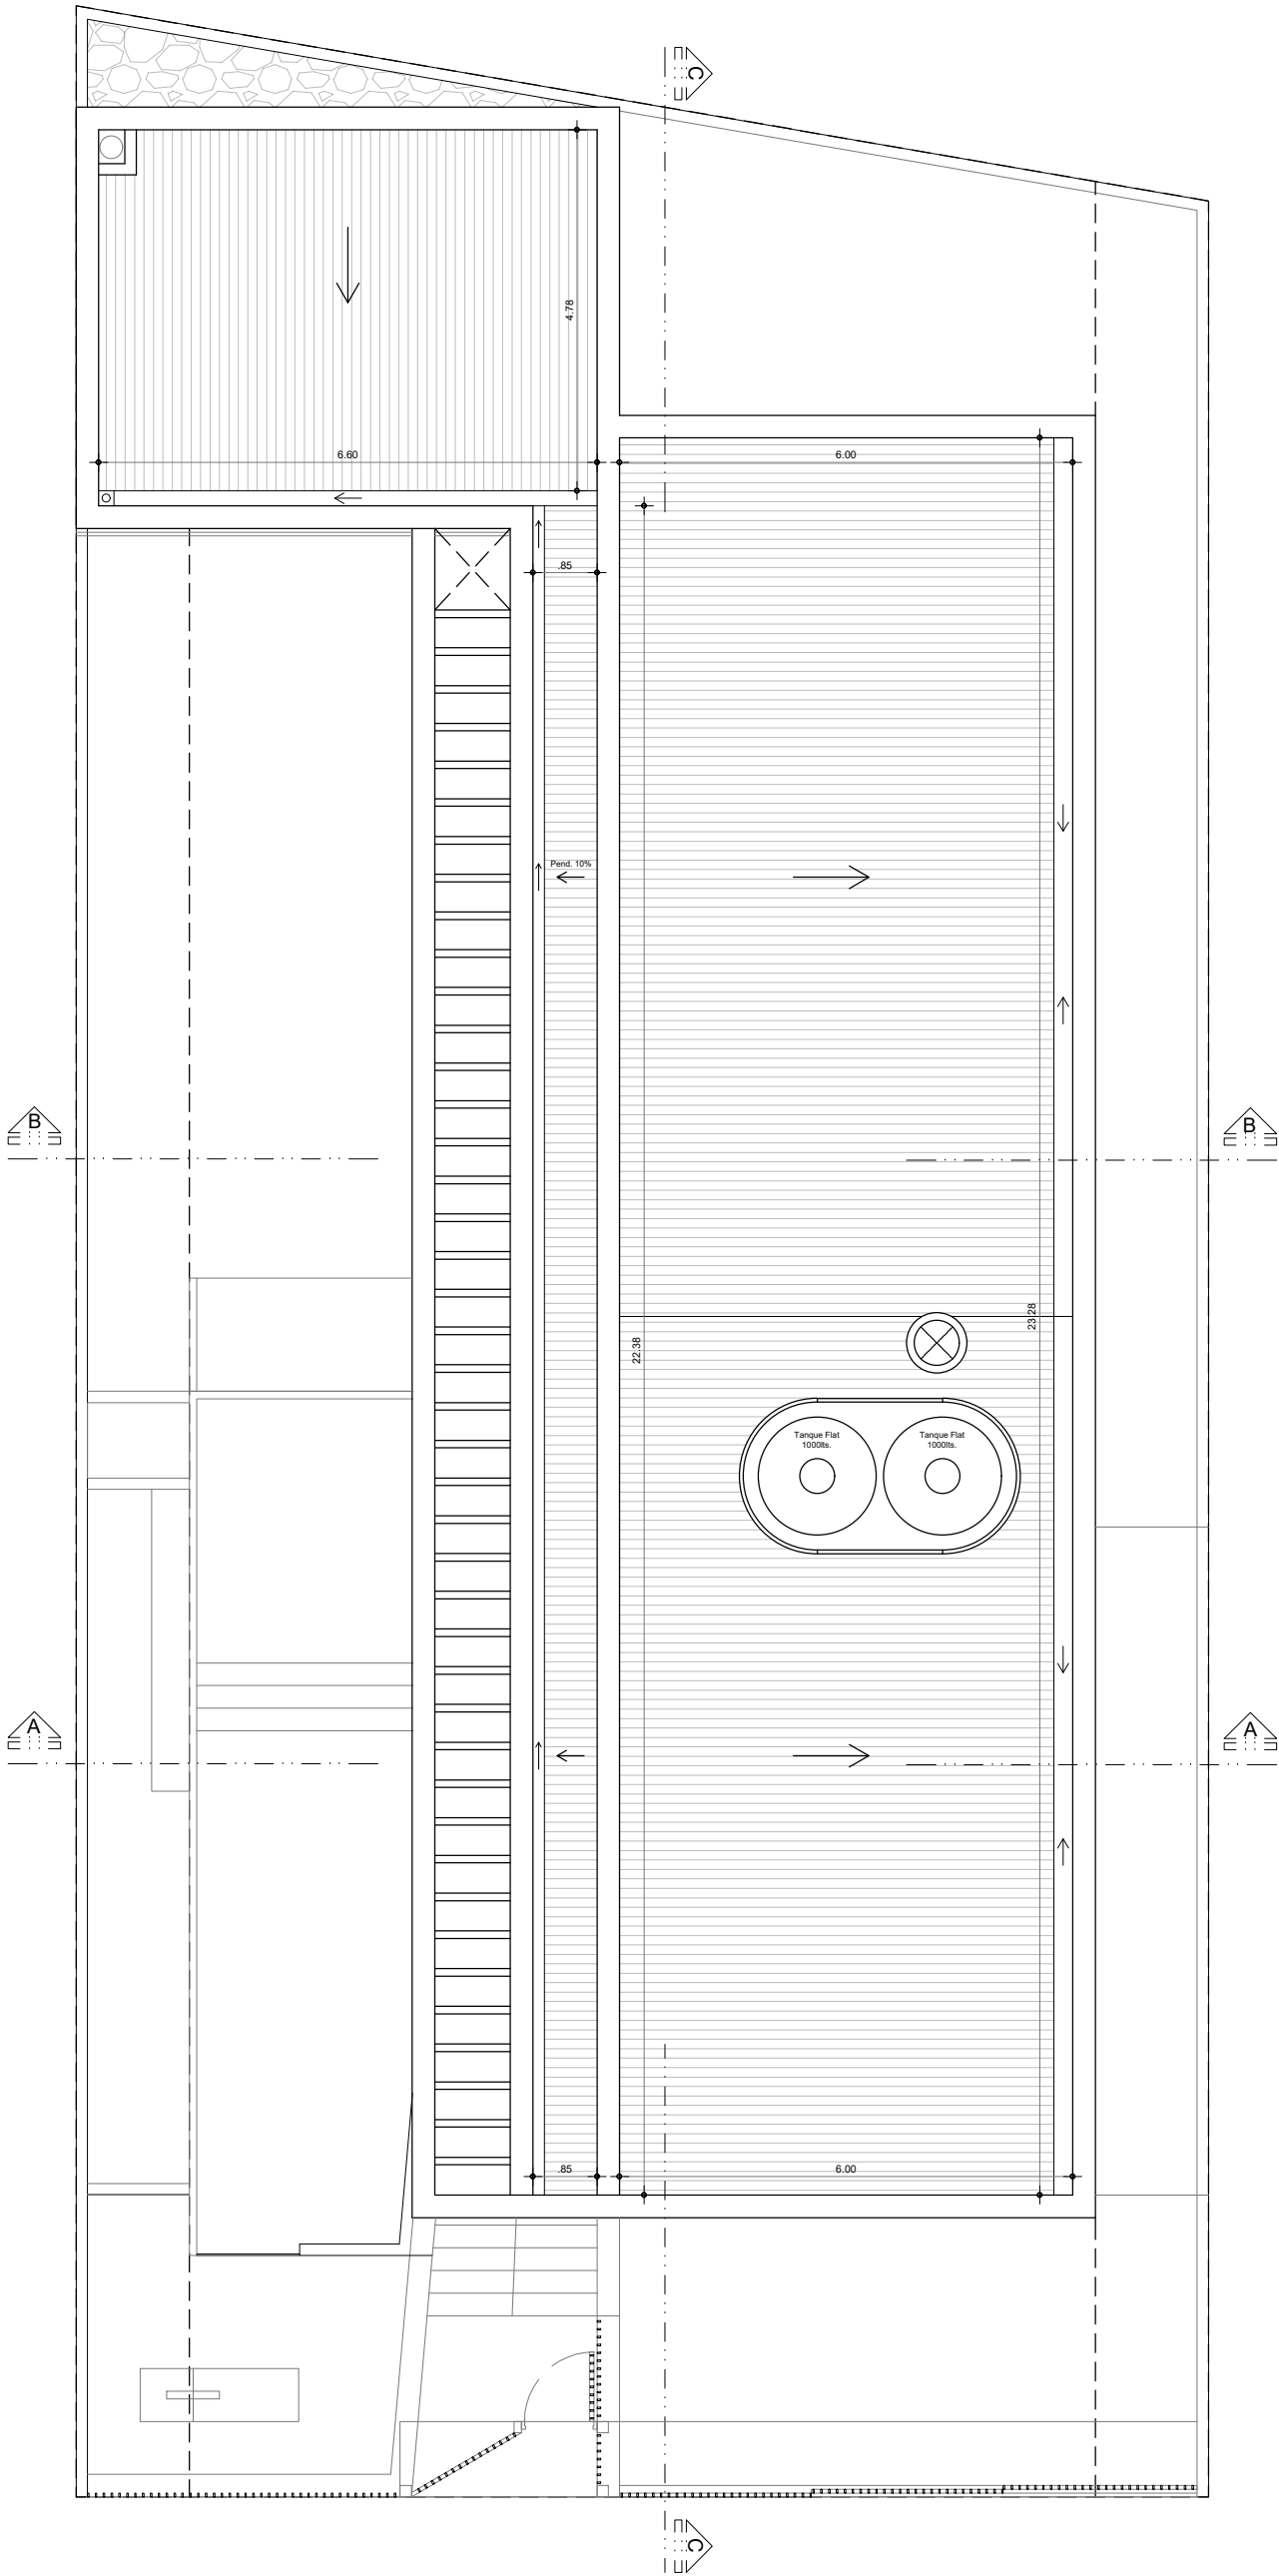

REFERANCIA COLUMNAS:
Propuestas
bajo tanques:

ESTUDIO MAPS
PROYECTO CASA EN LA CUESTA
Planta Techo ESCALA 1:100 - ARQUITECTURA EJECUTIVA

COMITENTE : BANDUCCI, German y GIUSIANO, Tatiana

2.1.4