1 D3

1 : 25

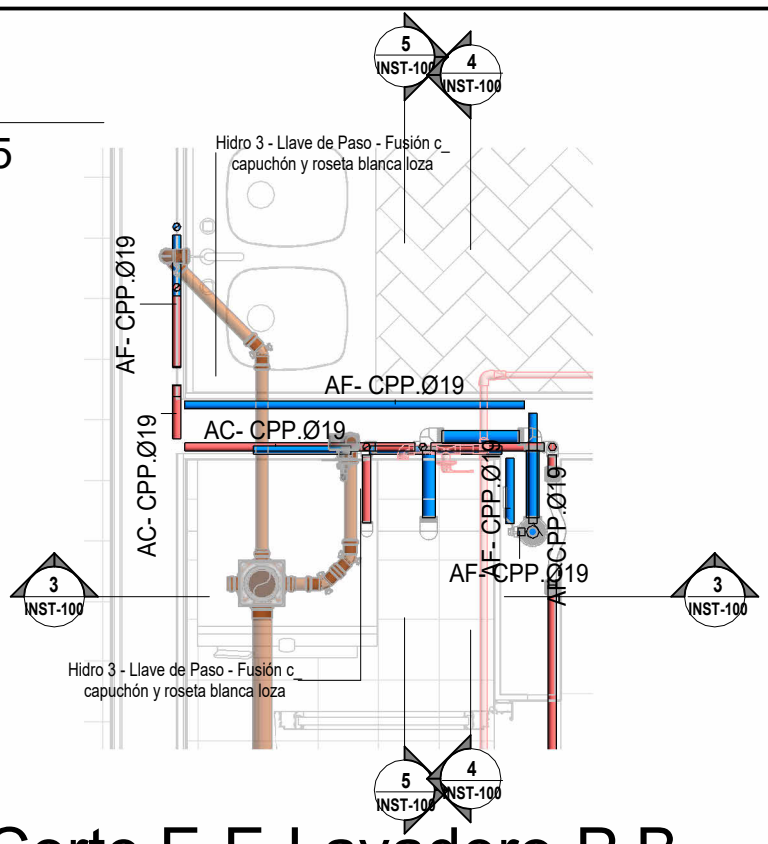

Corte E-E-Lavadero-P.B

3

1 : 25

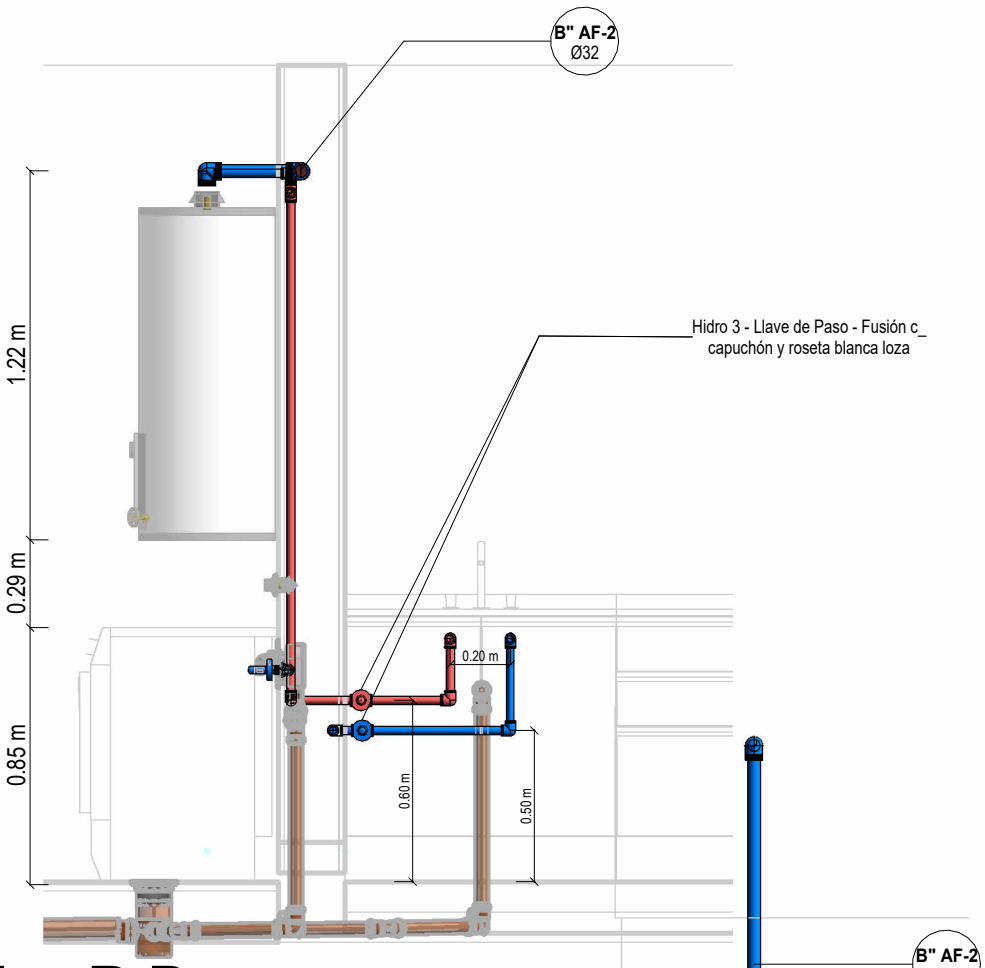

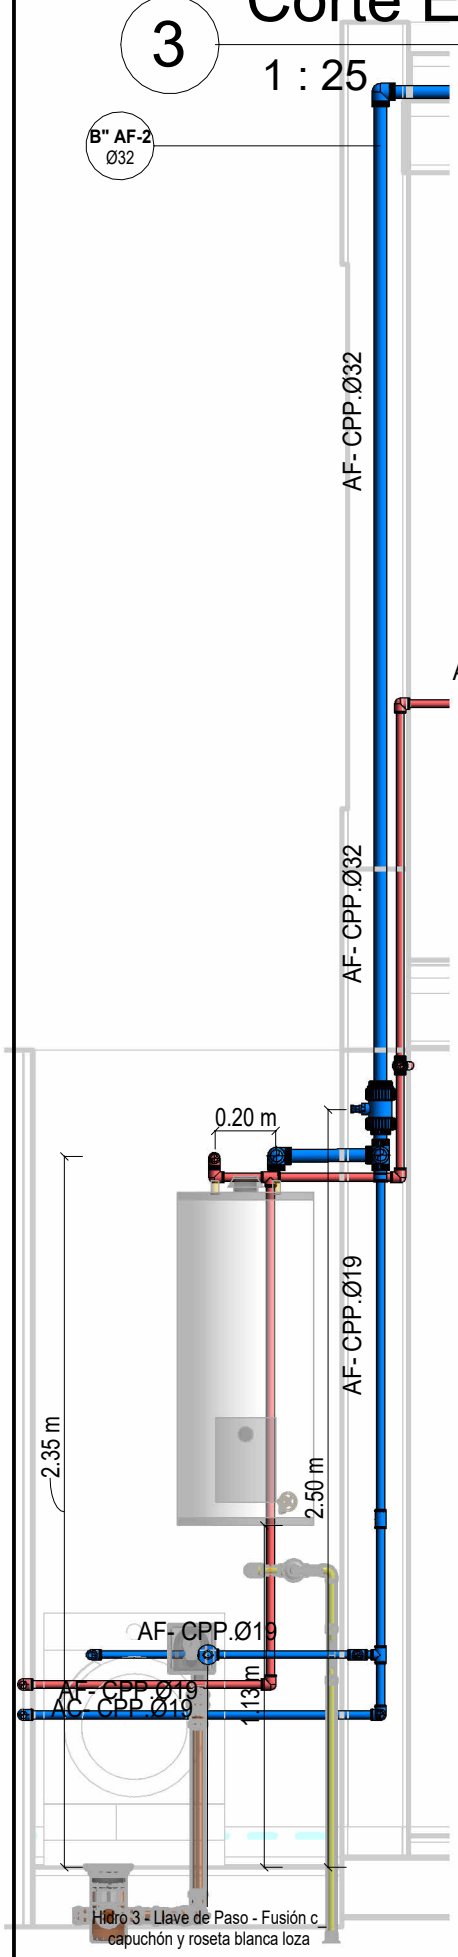

Corte F-F-1-Asador-P.B

4

1 : 25

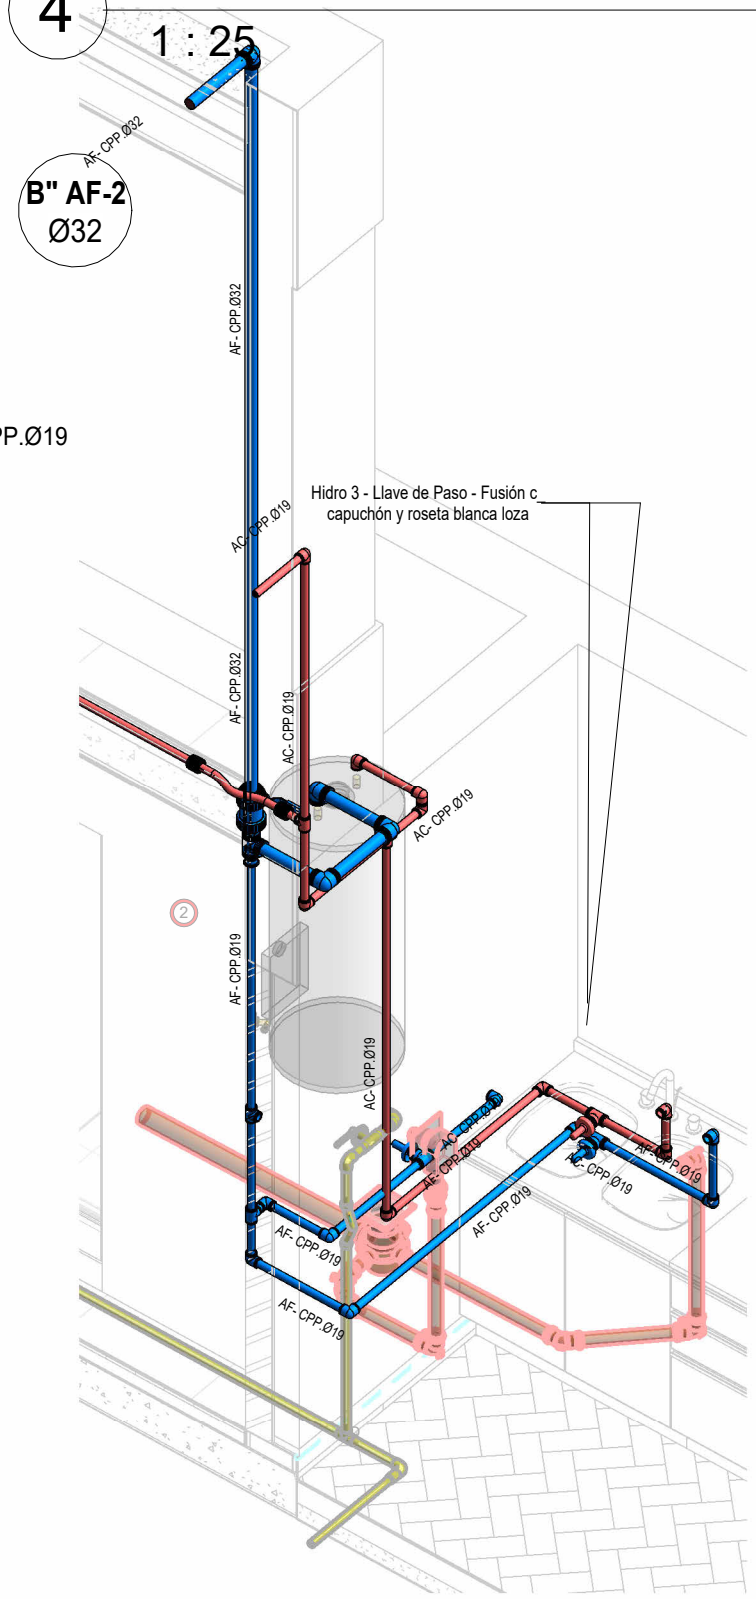

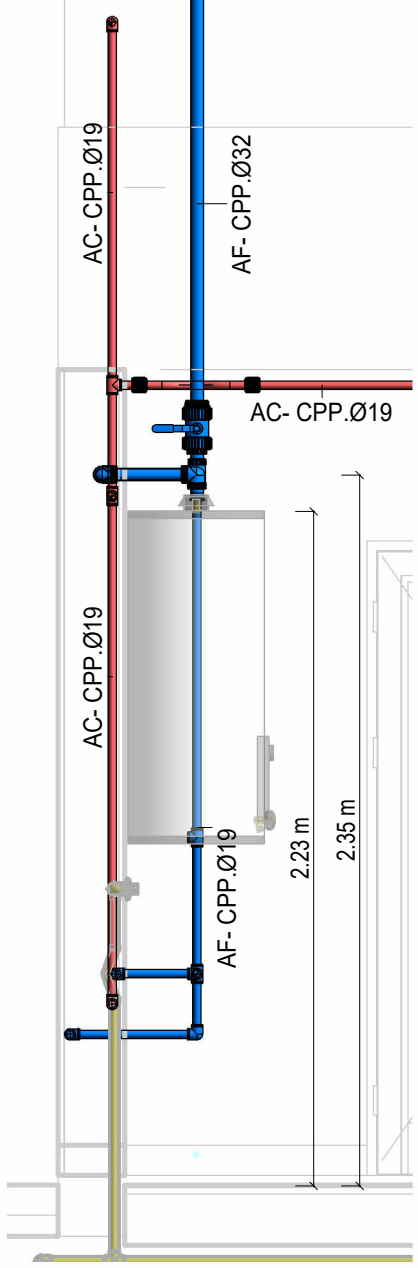

Axo-Lavadero/Asador

2

Corte A-A-Lavadero-P.B

5

1 : 25

14/5/2026 23:41:56

FGF ESTUDIO ARQUITECTURA

Propietario

Nombre de proyecto

Insta_Agua Fria/Caliente-Detalle-03

Número de proyecto	0001
Fecha	14/5/2026 23:41:56
Dibujado por	ARQ-Ferreyra
Comprobado por	ARQ-Ferreyra

INST-106

Escala 1 : 25